

RODINNÝ DŮM S ANTIKVARIÁTEM A KAVÁRNOU

STUDIE

RODINNÝ DŮM
S PROVOZOVNOU

místo VRANOVÉ II

investor DANIEL MULLER

arch. návrh ARCHITES

09/2025



ZÁMĚREM INVESTORA JE REKONSTRUKCE REKREAČNÍHO OBJEKTU Č. E. 663 NA PARC. ST. 127 V K. Ú. VRANOVÉ II

A ZMĚNA UŽÍVÁNÍ Z REKREAČNÍHO NA RODINNÝ DŮM S PROVOZOVNOU.

STÁVAJÍCÍ DŮM JE CHARAKTERISTICKÝ NÁROŽNÍM RIZALITEM ORIENTOVANÝM K HLAVNÍ SILNICI A ŘECE, TEDY SMĚREM K LOKÁLNÍMU CENTRU.

NÁVRH OBNOVUJE HISTORICKY PŮVODNÍ VSTUP DO PROVOZOVNY V PŘÍZEMÍ RIZALITU. PRODEJNÍ ČÁST JE SITUOVÁNA DO VÝCHODNÍ ČÁSTI PŘÍZEMÍ,

V ZÁPADNÍ ČÁSTI SE NACHÁZÍ VSTUP A GARÁŽ NÁLEŽEJÍCÍ K BYTU V PODKROVÍ. BYT JE VELIKOSTI 5+KK S MALÝM ATRIEM A STŘEŠNÍ TERASOU NAD ZÁPADNÍ ČÁSTÍ DOMU.

VÝCHODNÍ ČÁST OBJEKTU, POHLEDOVĚ VÍCE EXPONOVANÁ, ZACHOVÁVÁ CHARAKTER PŮVODNÍ STAVBY – DŮM SE SEDLOVOU STŘECHOU A NÁROŽNÍM RIZALITEM.

ZÁPADNÍ ČÁST MÁ MODERNÍ VÝRAZ JEDNODUCHÉHO KVÁDRU S DŘEVĚNOU FASÁDOU.

VÝSLEDNÉ KAPACITY:

- BYTOVÁ ČÁST: KOMFORTNÍ BYT 5+KK S VLASTNÍ GARÁŽÍ, UŽITNÁ PLOCHA BYTU CELKEM 190 m², TERASY CELKEM 52 m².
- PROVOZOVNA: PRODEJNÍ PROSTOR SE SKLADEM A SOCIÁLNÍM ZAŘÍZENÍM, UŽITNÁ PLOCHA 70 m².

STAVEBNĚ-TECHNICKÉ ŘEŠENÍ:

- ZÁKLADY A SUTERÉN/PŘÍZEMÍ:

ZALOŽENÍ STAVBY STÁVAJÍCÍ

NOVÉ HYDROIZOLACE STĚN A PODLAH,

NOVÉ HRUBÉ PODLAHY VČETNĚ TEPELNÉ IZOLACE.

- NOSNÉ SVISLÉ KONSTRUKCE:

NOSNÉ ZDIVO STÁVAJÍCÍ,

POŠKOZENÉ ČÁSTI BUDOU OPRAVENY

NEBO ZNOVUVYZDĚNY Z KERAMICKÝCH TVÁRNIC

OBVODOVÉ STĚNY DOPLNĚNY O TEPELNOU IZOLACI

- STROPY:

STÁVAJÍCÍ STROPY NAD PŘÍZEMÍM NAHRADÍ

NOVÉ ŽELEZOBETONOVÉ KONSTRUKCE

S OCELOVÝMI PRŮVLAKY

- KROV A STŘECHY:

SEDLOVÁ STŘECHA S TRADIČNÍM KROVEM

S POHLEDOVÝMI PRVKY V INTERIÉRU PODKROVÍ, NADKROKEVNÍ TEPELNÁ IZOLACE.

PLOCHÉ STŘECHY S DŘEVĚNOU KONSTRUKCÍ

POVRCHY:

VÝCHODNÍ ČÁST – OMÍTANÁ FASÁDA, SEDLOVÁ STŘECHA S KRYTINOU Z FALCOVANÉHO PLECHU.

ZÁPADNÍ ČÁST – DŘEVĚNÁ FASÁDA, PLOCHÉ STŘECHY S HYDROIZOLACÍ Z FÓLIE EPDM, SVISLÉ OPLECHOVÁNÍ PODKROVNÍCH STĚN FALCOVANÝM PLECHEM

TERASA ŘEŠENA JAKO TZV. OBRÁCENÁ STŘECHA.

- TECHNICKÉ VYBAVENÍ: NAPOJENÍ NA ELEKTRICKOU SÍŤ, VEŘEJNÝ VODOVOD A OBECNÍ KANALIZACI.

VYTÁPĚNÍ ELEKTROKOTLEM S PODLAHOVÝM TOPENÍM. DO BUDOUCNA JE UVAŽOVÁNA INSTALACE FVE NA JIŽNÍ STŘEŠNÍ ROVINU.

Z Á M Ě R



RODINNÝ DŮM S PROVOZOVNOU
VRANOVÉ II 09-2025

SITUACE

M 1:250

Vranové 2. díl

RODINNÝ DŮM S PROVOZOVNOU
VRANOVÉ II


09-2025


ARCHITES

PŮDORYS

1.NP

M 1:75

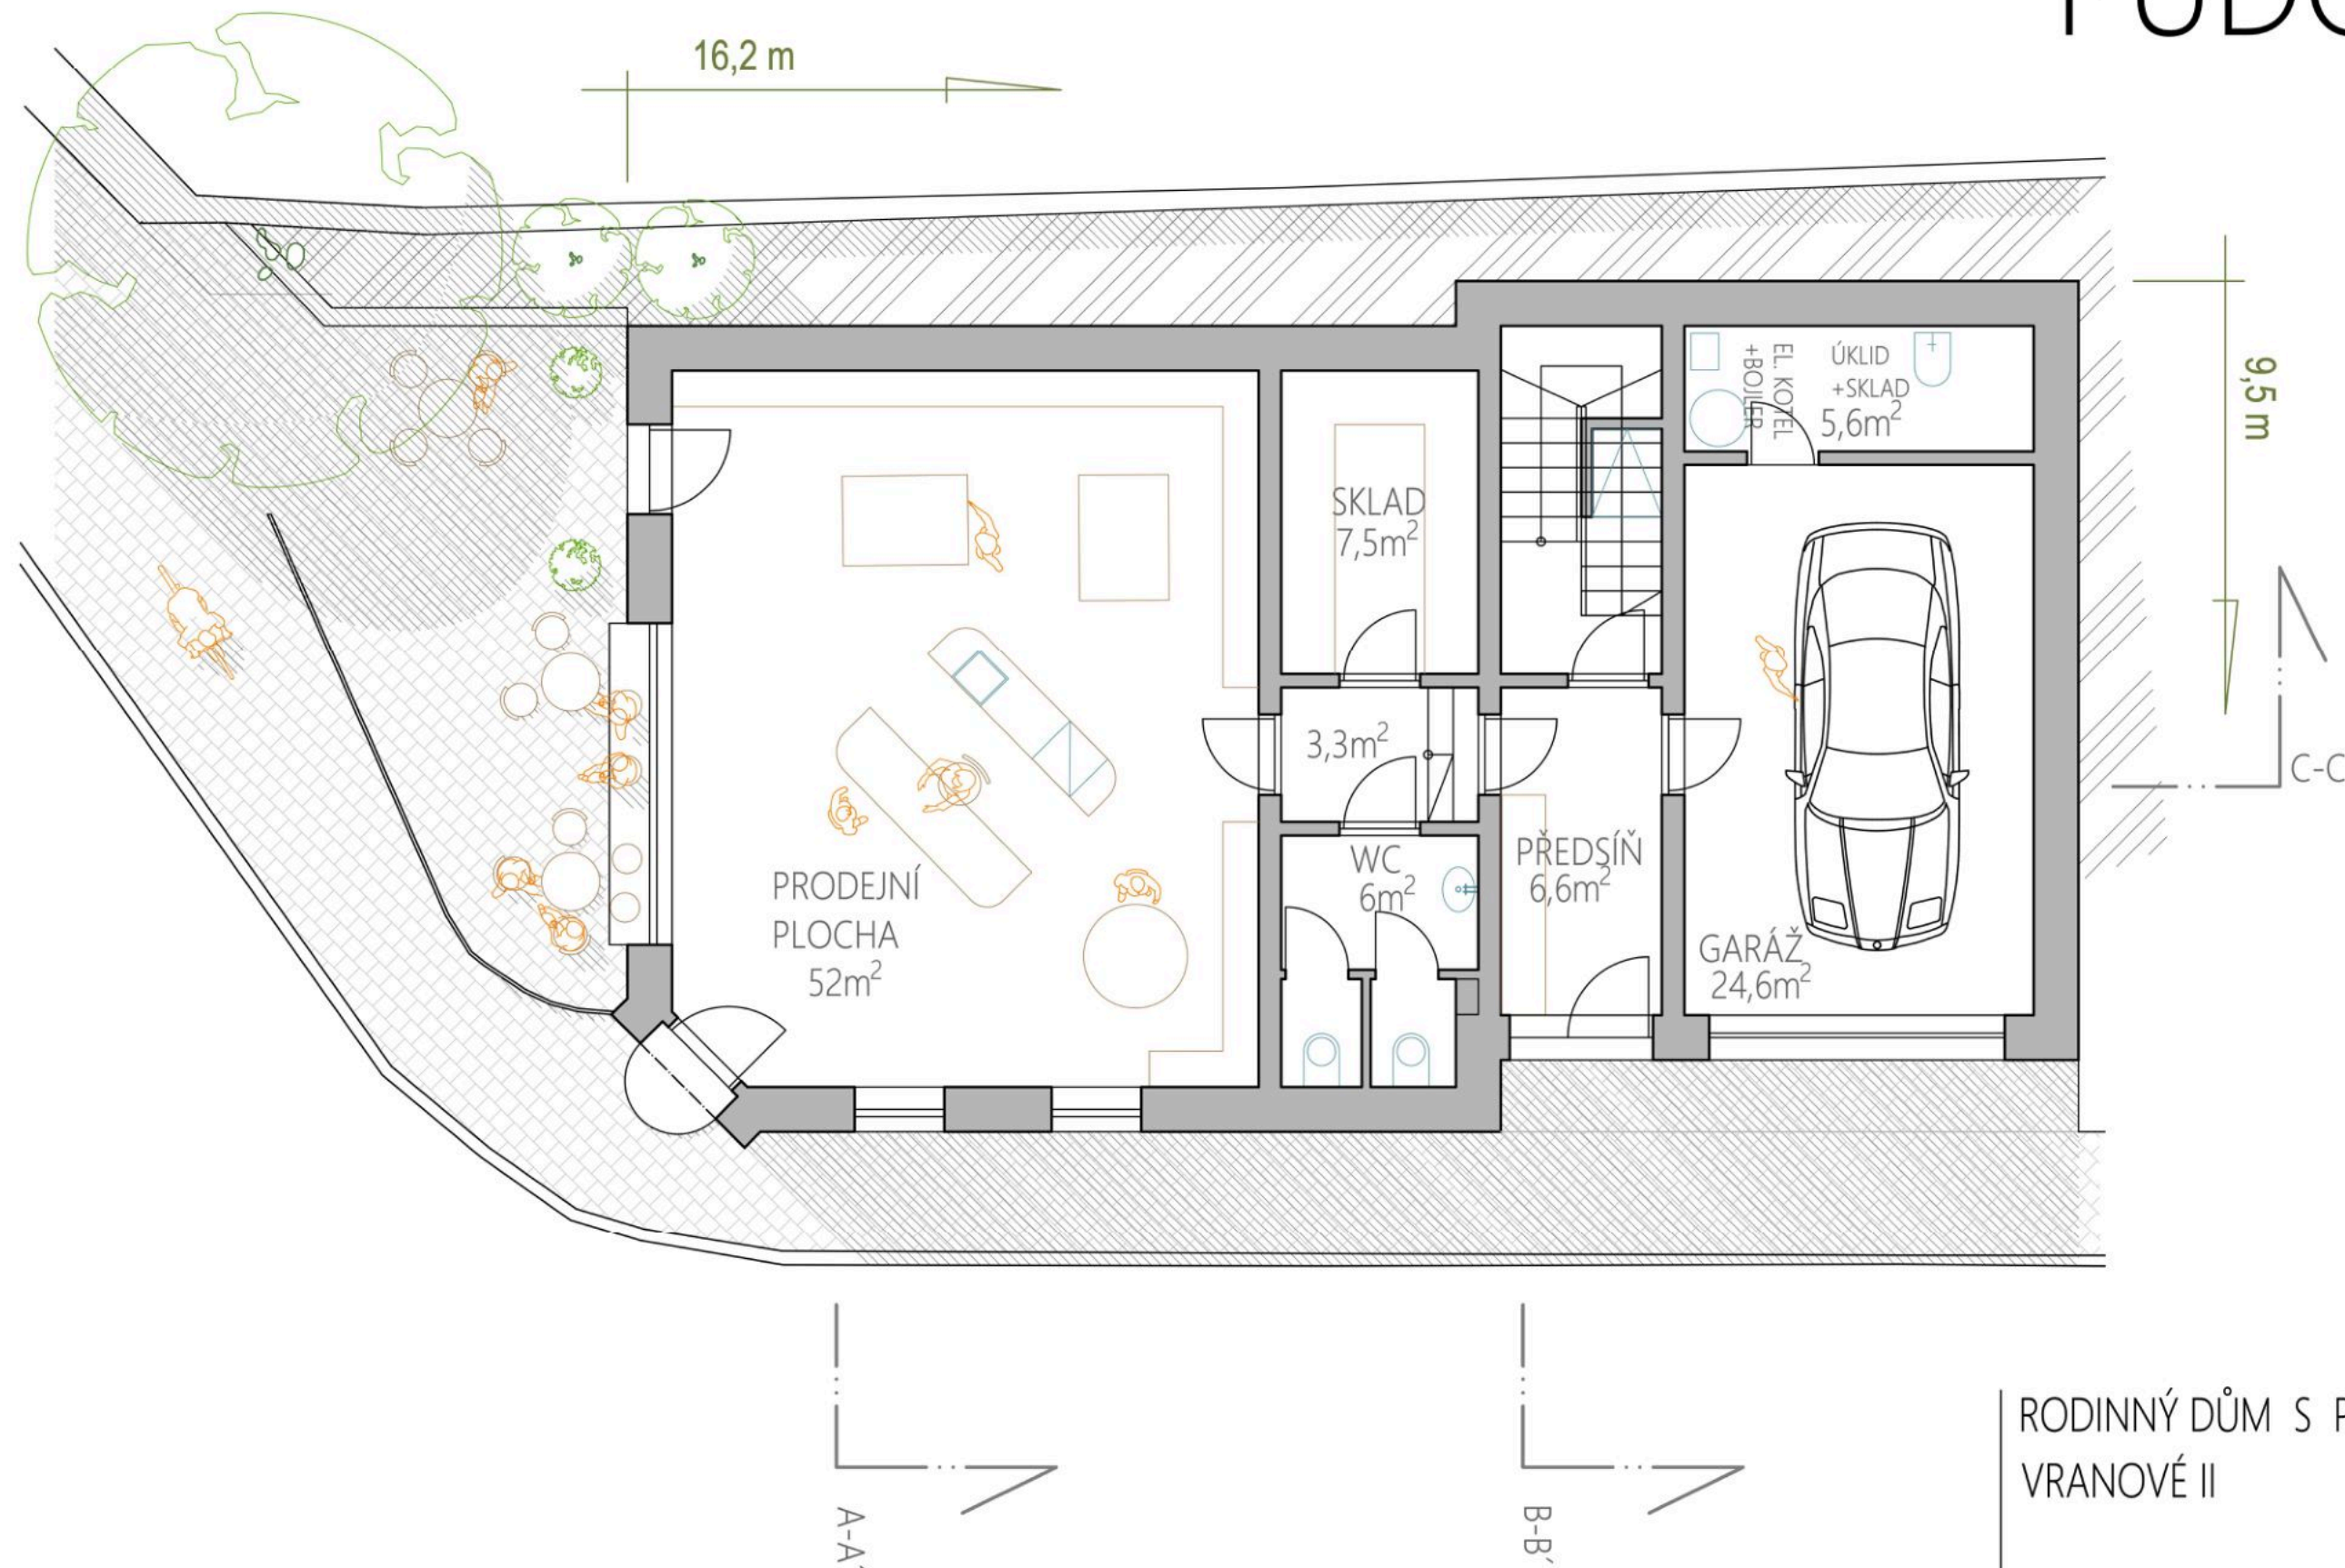


RODINNÝ DŮM S PROVOZOVNOU
VRANOVÉ II
09-2025

PŮDORYS

2.NP


M 1:75

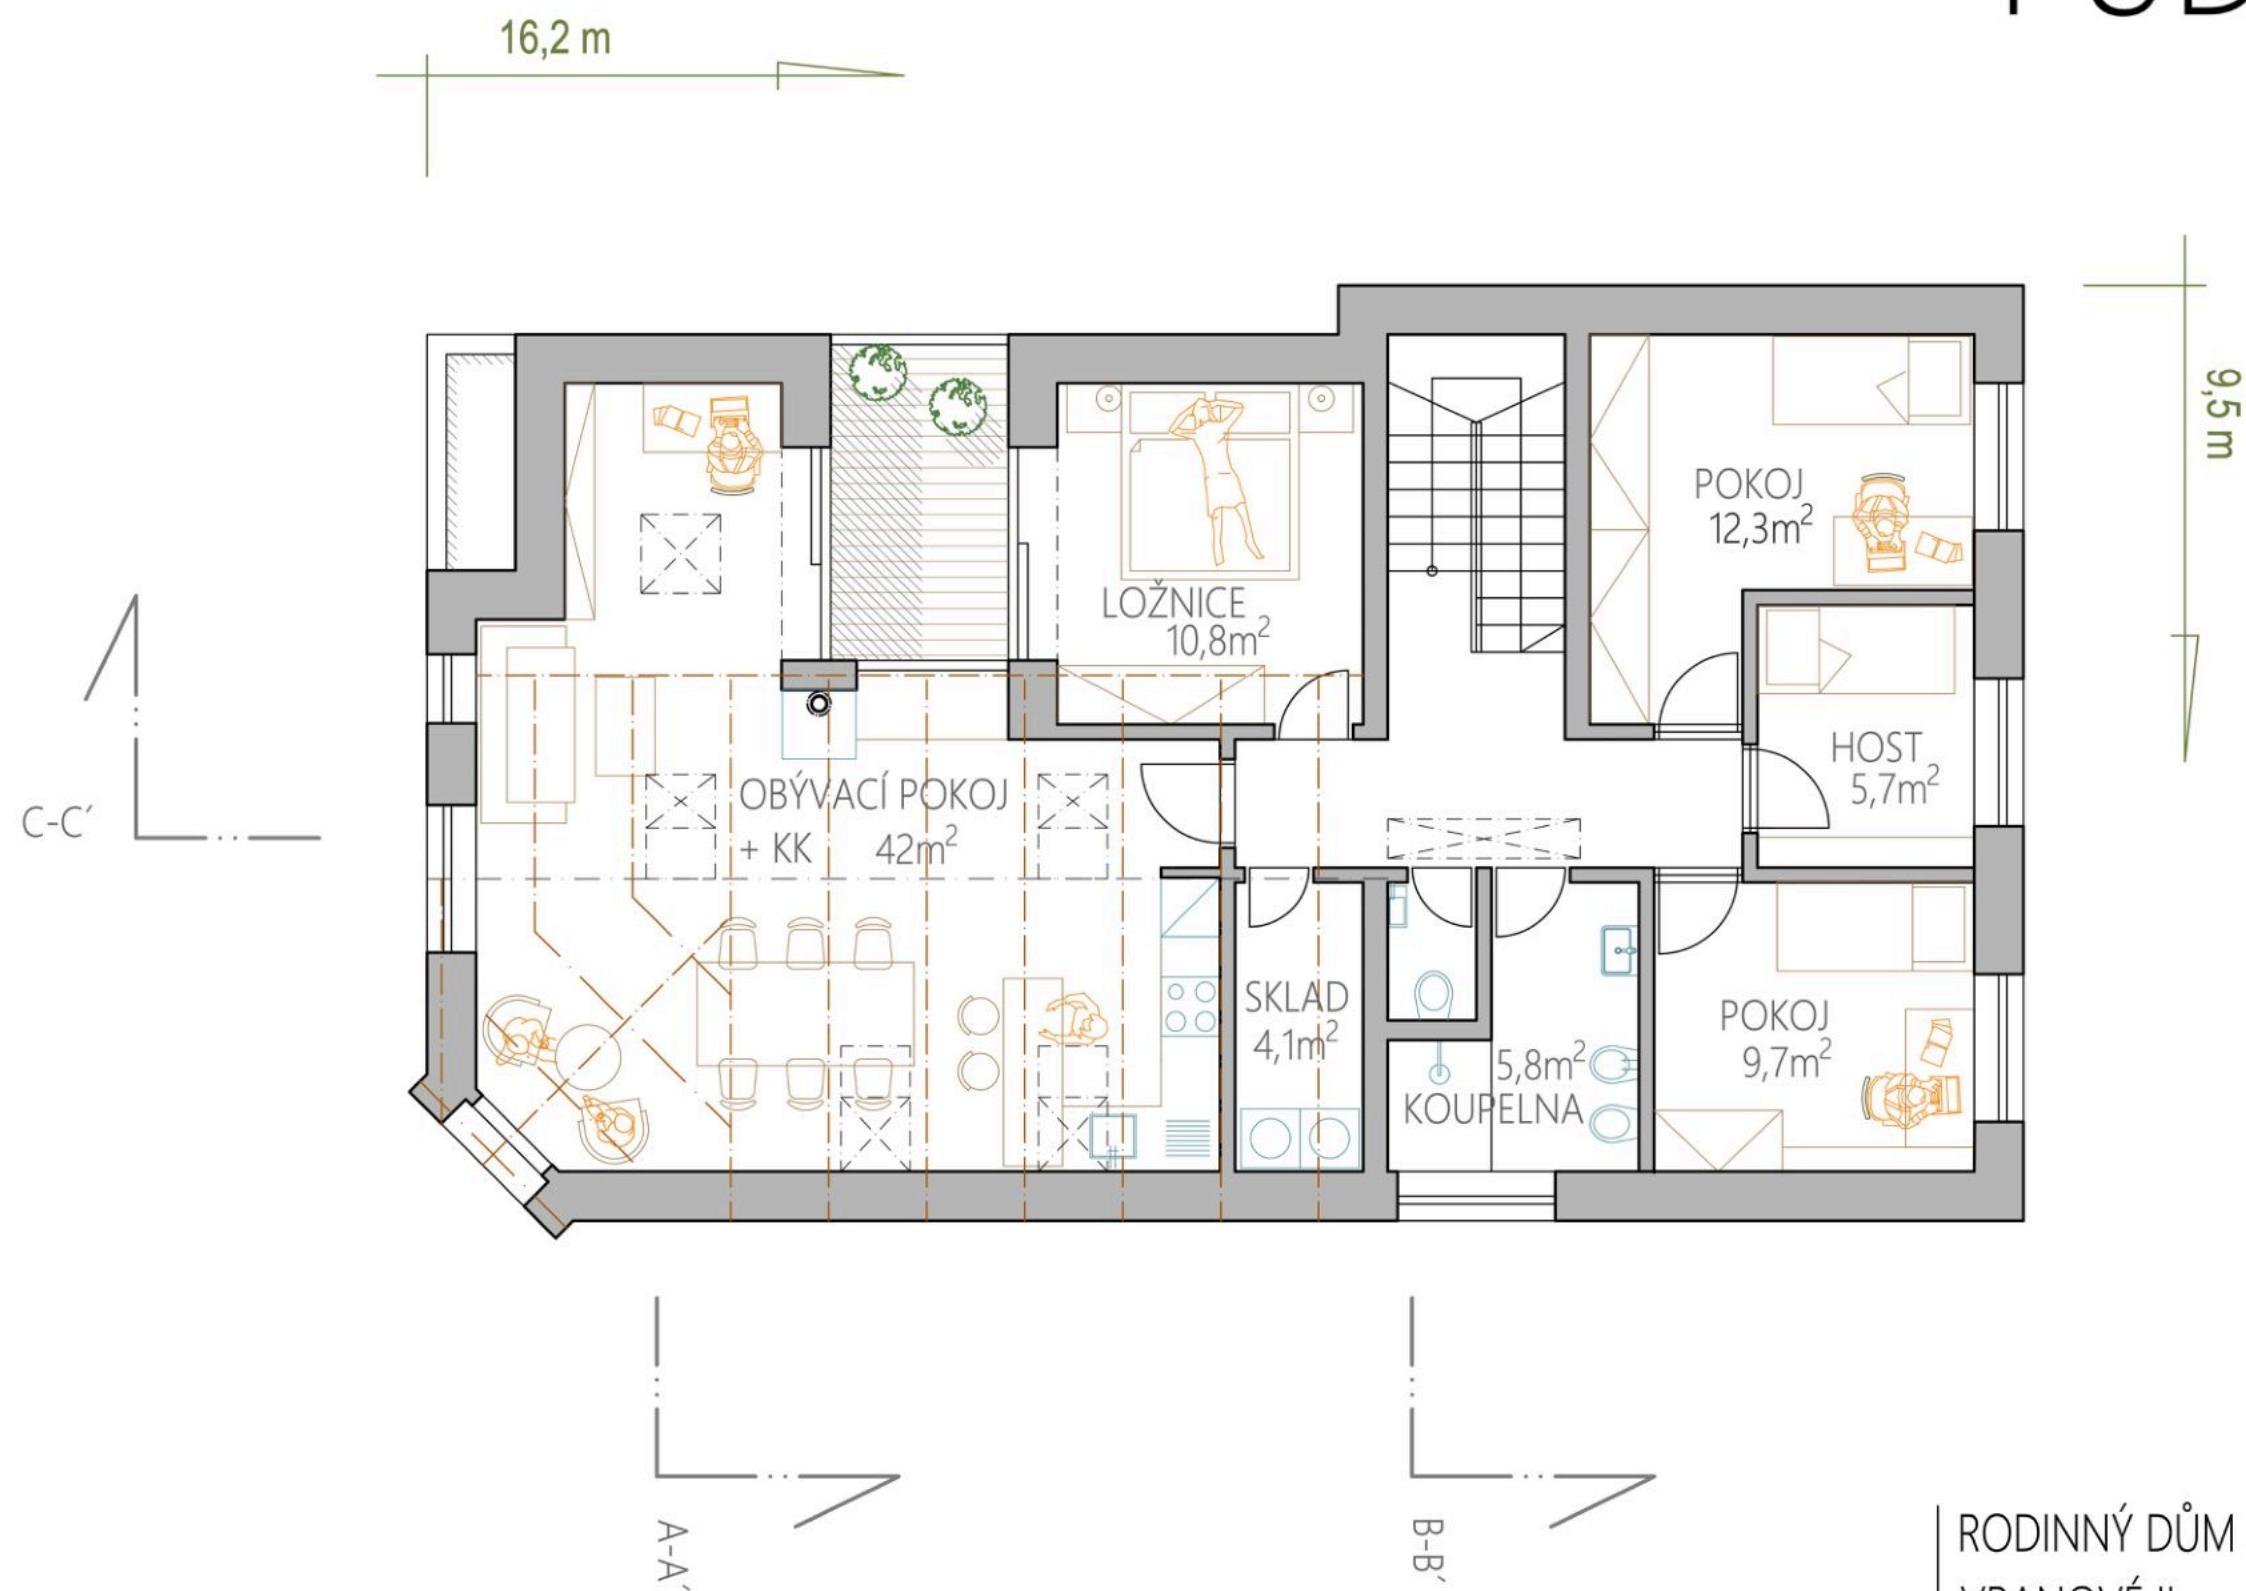

RODINNÝ DŮM S PROVOZOVNOU
VRANOVÉ II 09-2025

PŮDORYS STŘECHY


M 1:75

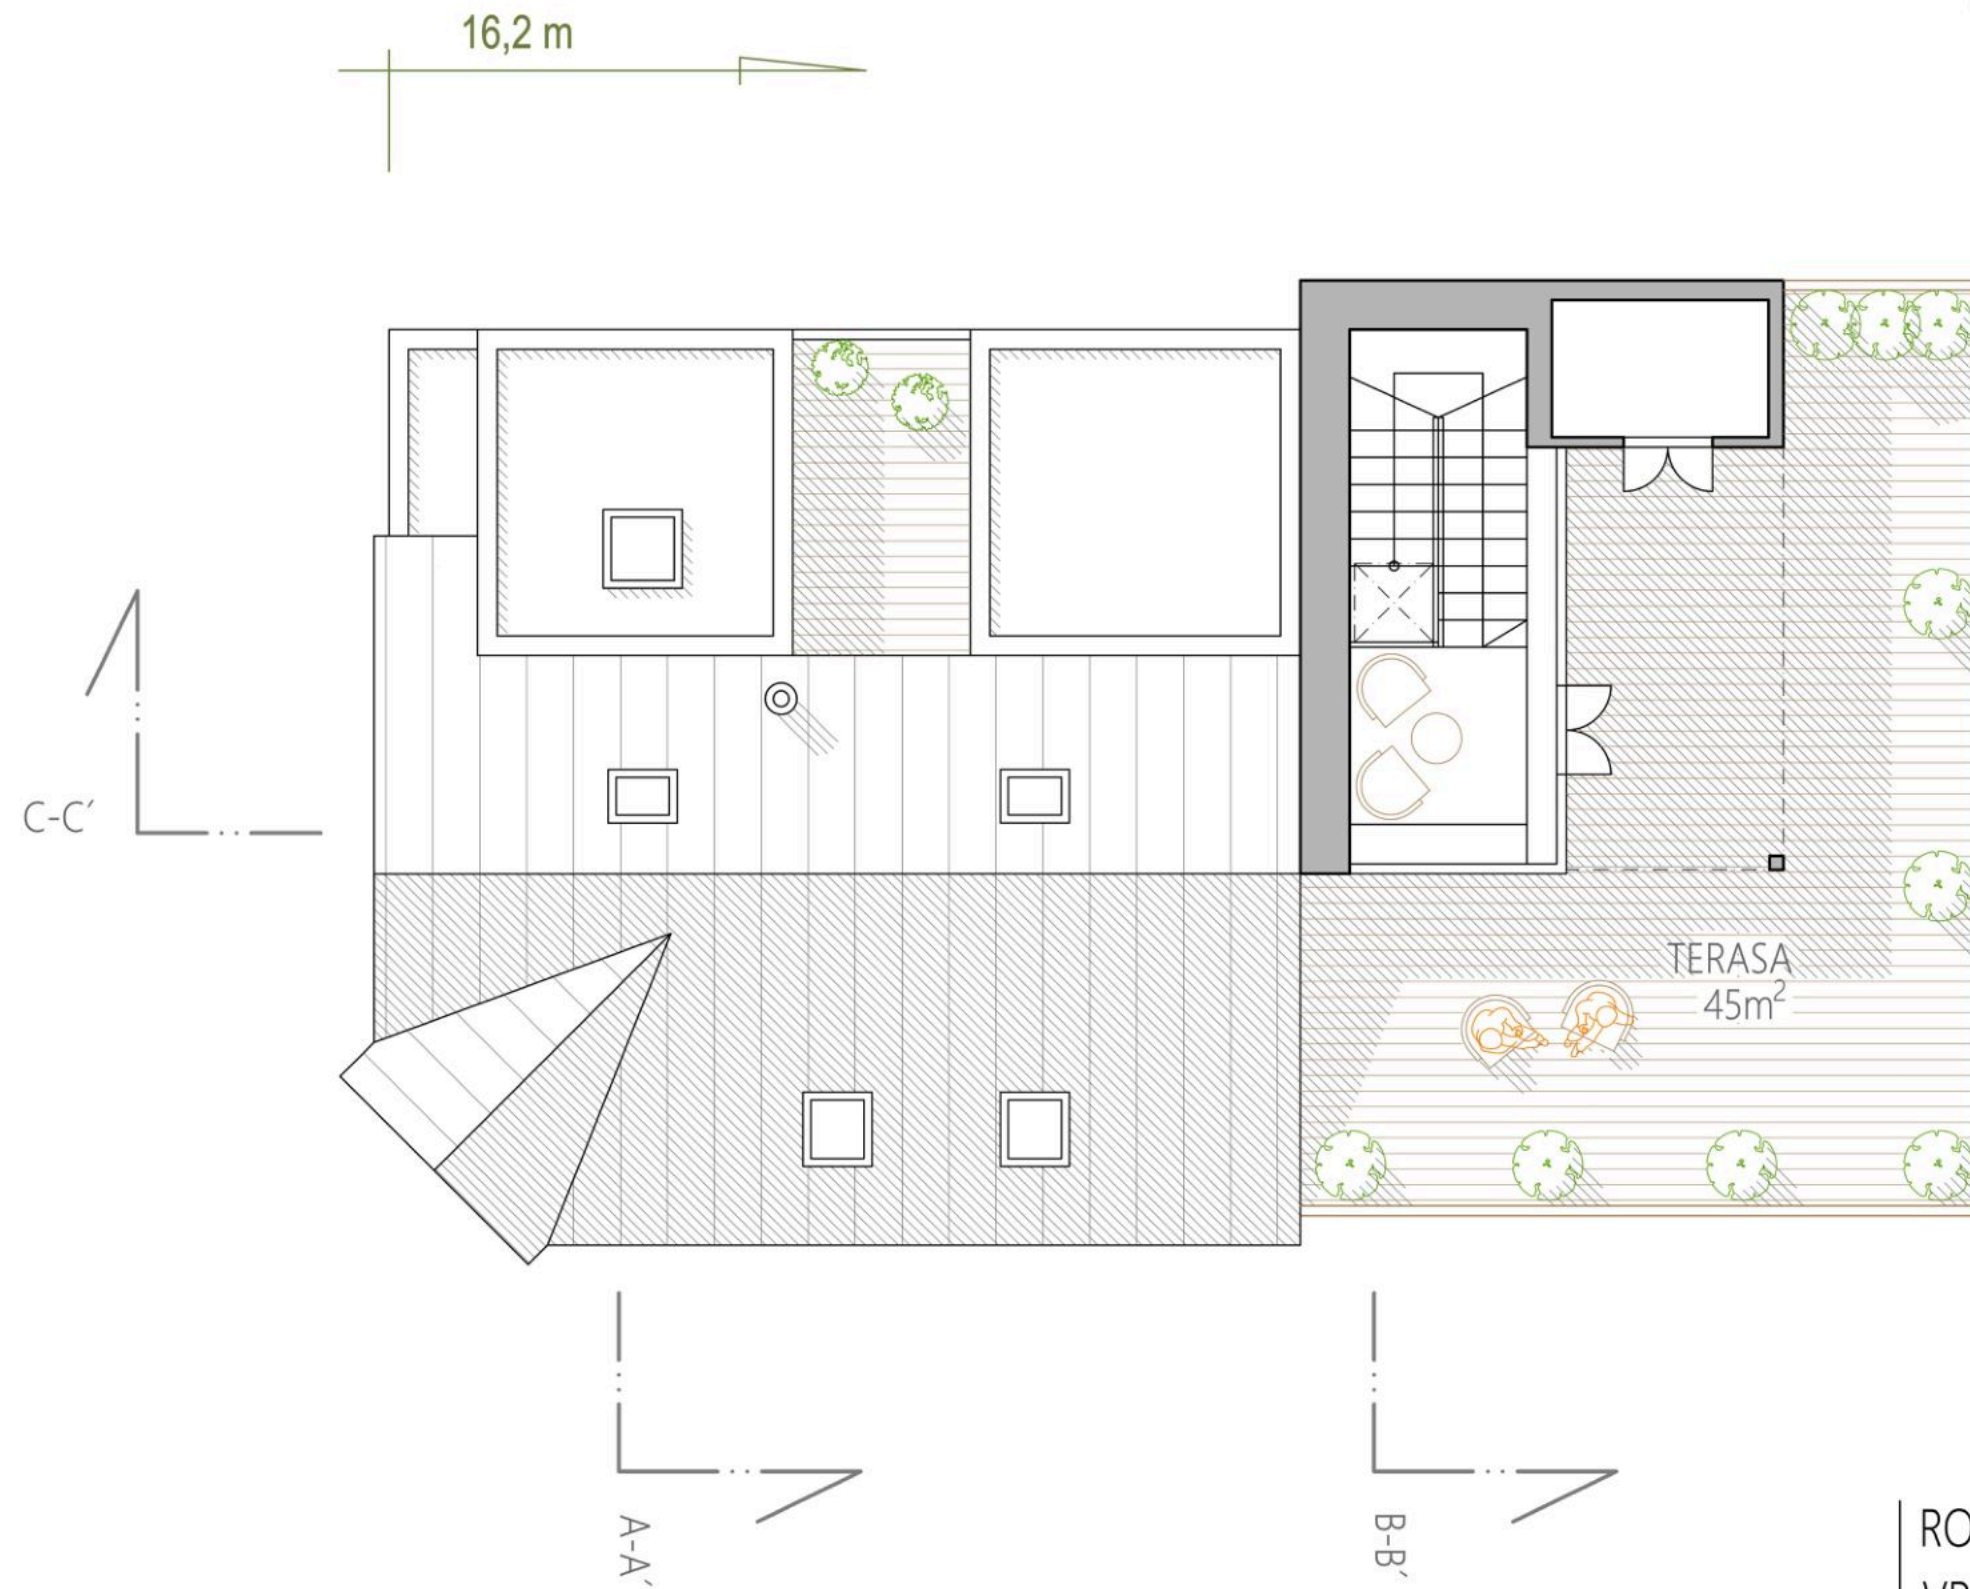

RODINNÝ DŮM S PROVOZOVNOU
VRANOVÉ II 09-2025

PŘÍČNÝ ŘEZ A-A'


M 1:75

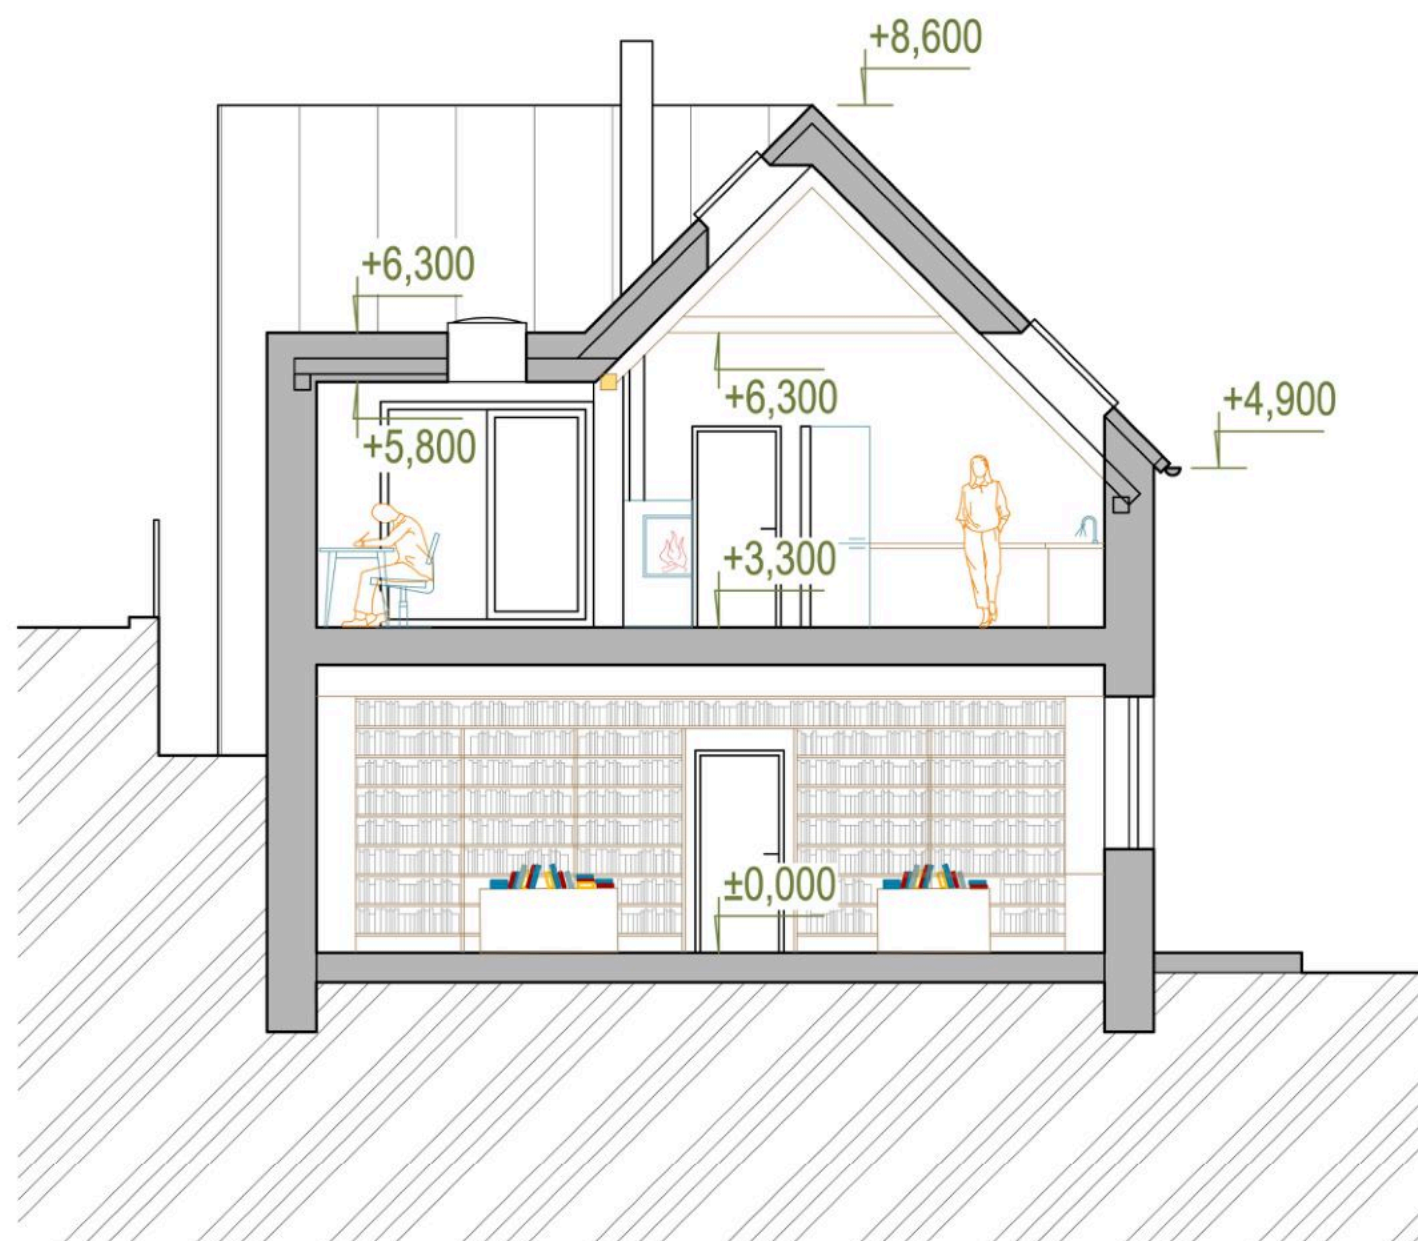

RODINNÝ DŮM S PROVOZOVNOU
VRANOVÉ II 09-2025

PŘÍČNÝ ŘEZ B-B'


M 1:75

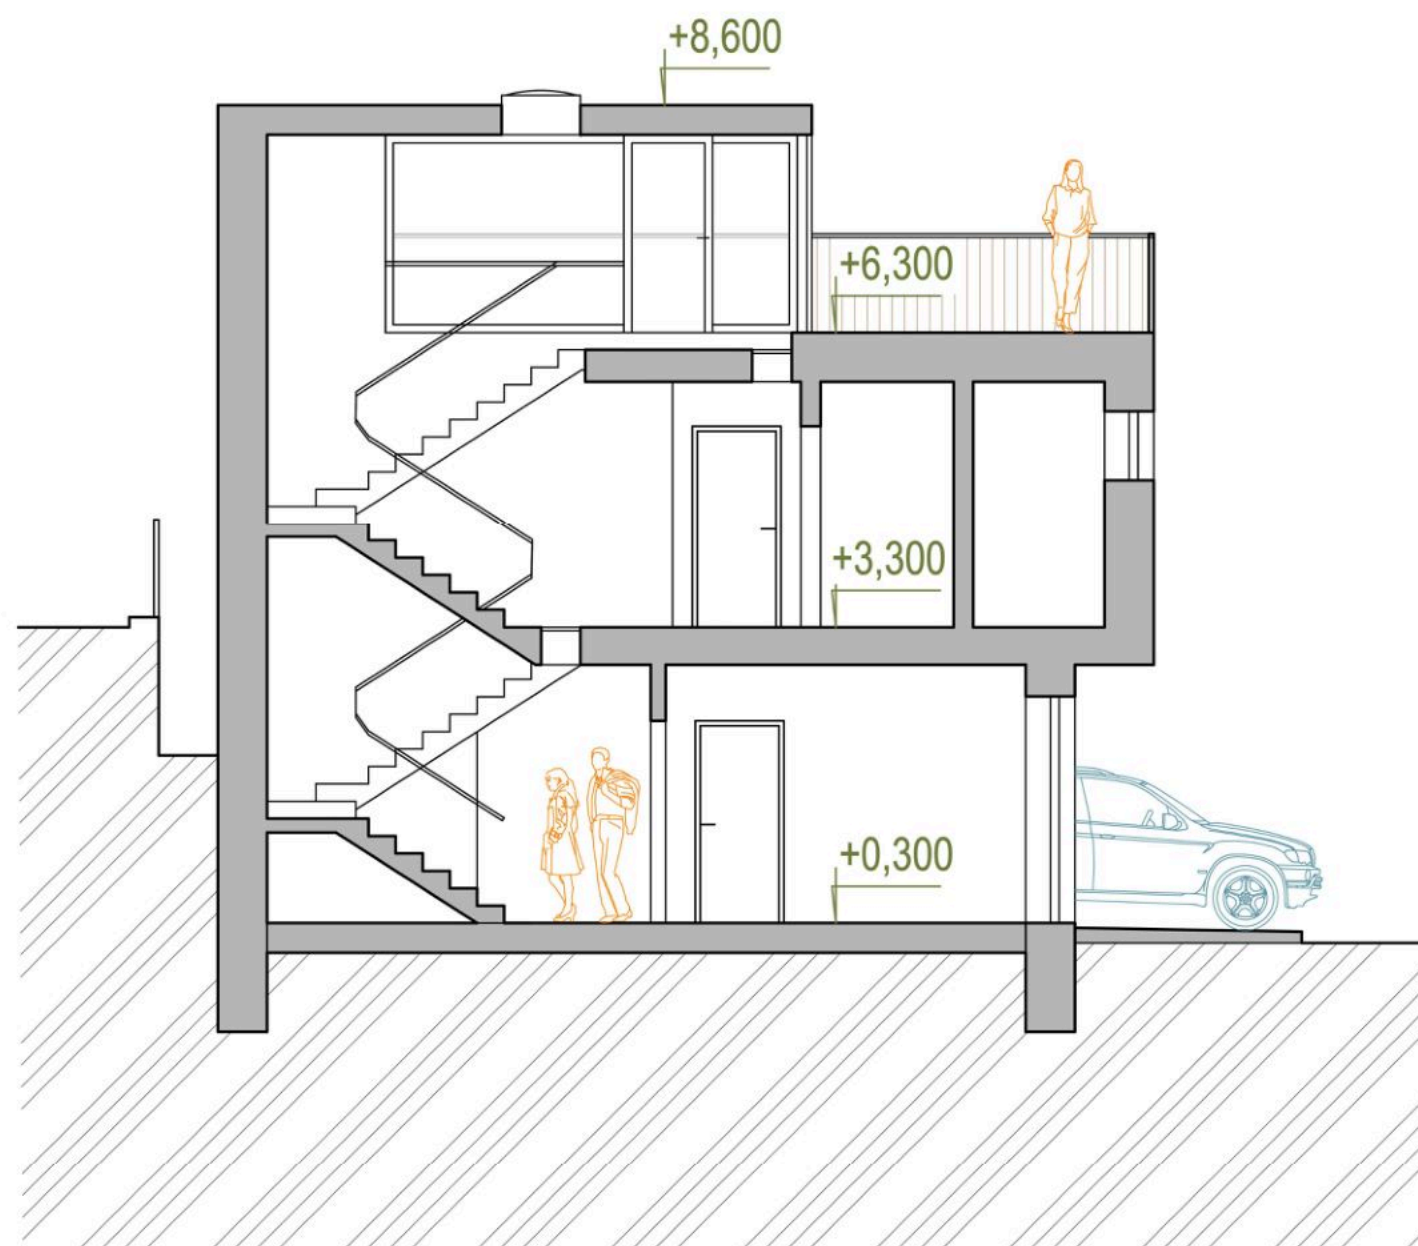

RODINNÝ DŮM S PROVOZOVNOU
VRANOVÉ II 09-2025

PŘÍČNÝ ŘEZ C-C'

M 1:75

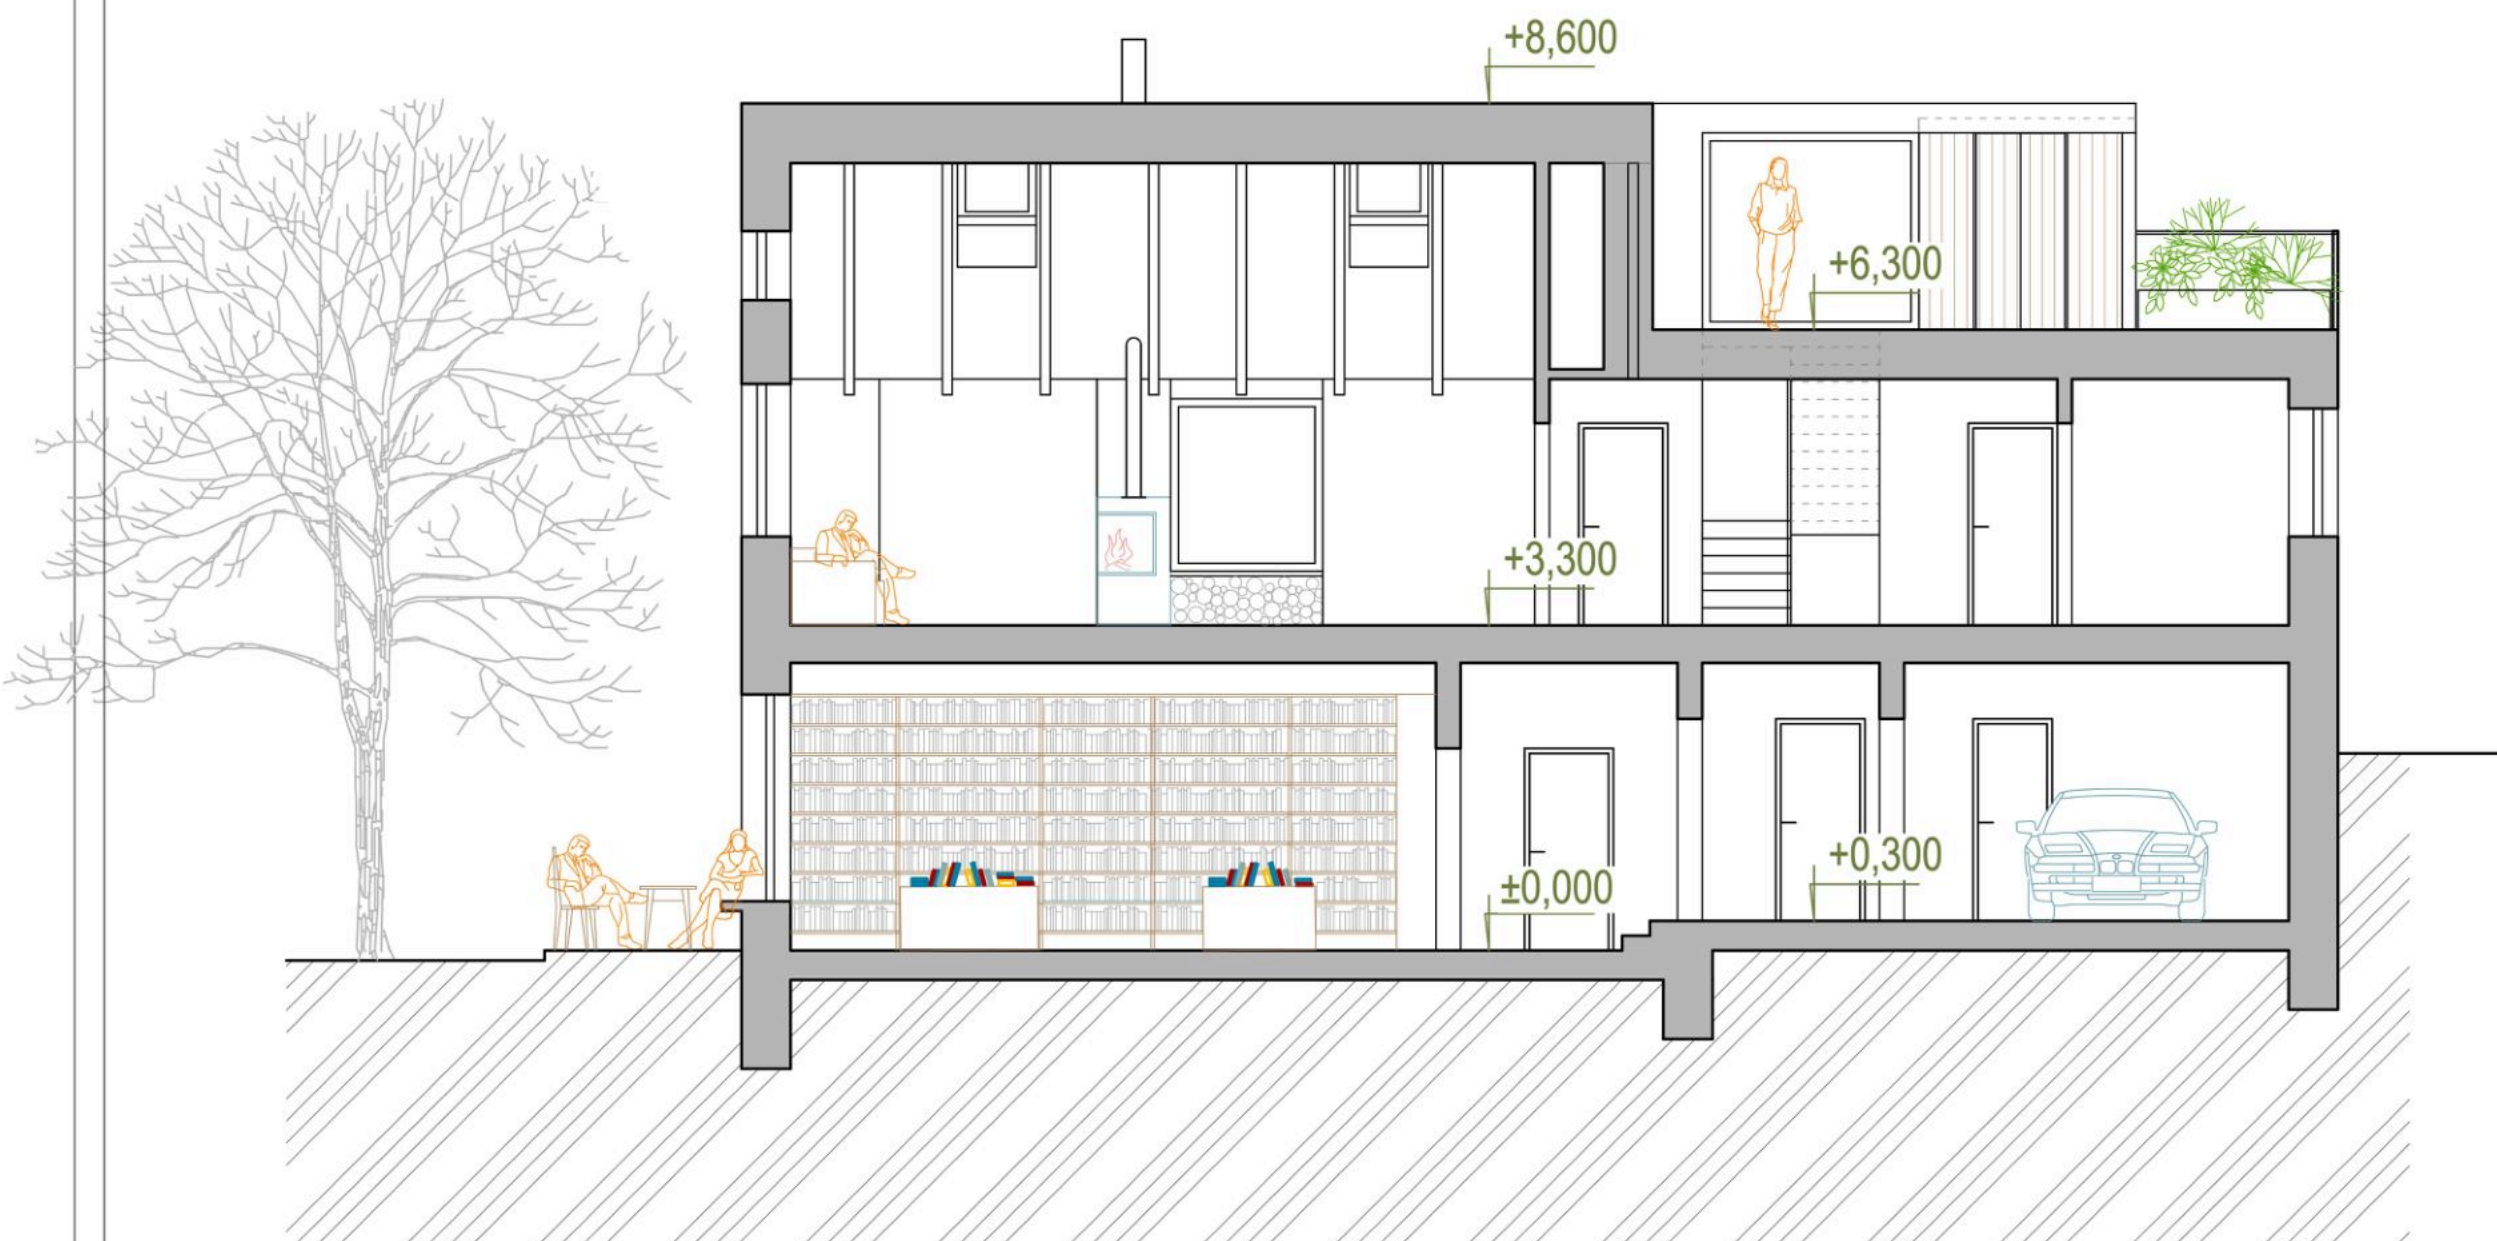

RODINNÝ DŮM S PROVOZOVNOU
VRANOVÉ II 09-2025

POHLED VÝCHODNÍ

M 1:75



RODINNÝ DŮM S PROVOZOVNOU
VRANOVÉ II 09-2025

POHLED SEVERNÍ

M 1:75



RODINNÝ DŮM S PROVOZOVNOU
VRANOVÉ II 09-2025

POHLED ZÁPADNÍ

M 1:75



RODINNÝ DŮM S PROVOZOVNOU
VRANOVÉ II 09-2025


POHLED JIŽNÍ

M 1:75



RODINNÝ DŮM S PROVOZOVNOU
VRANOVÉ II 09-2025

MODEL

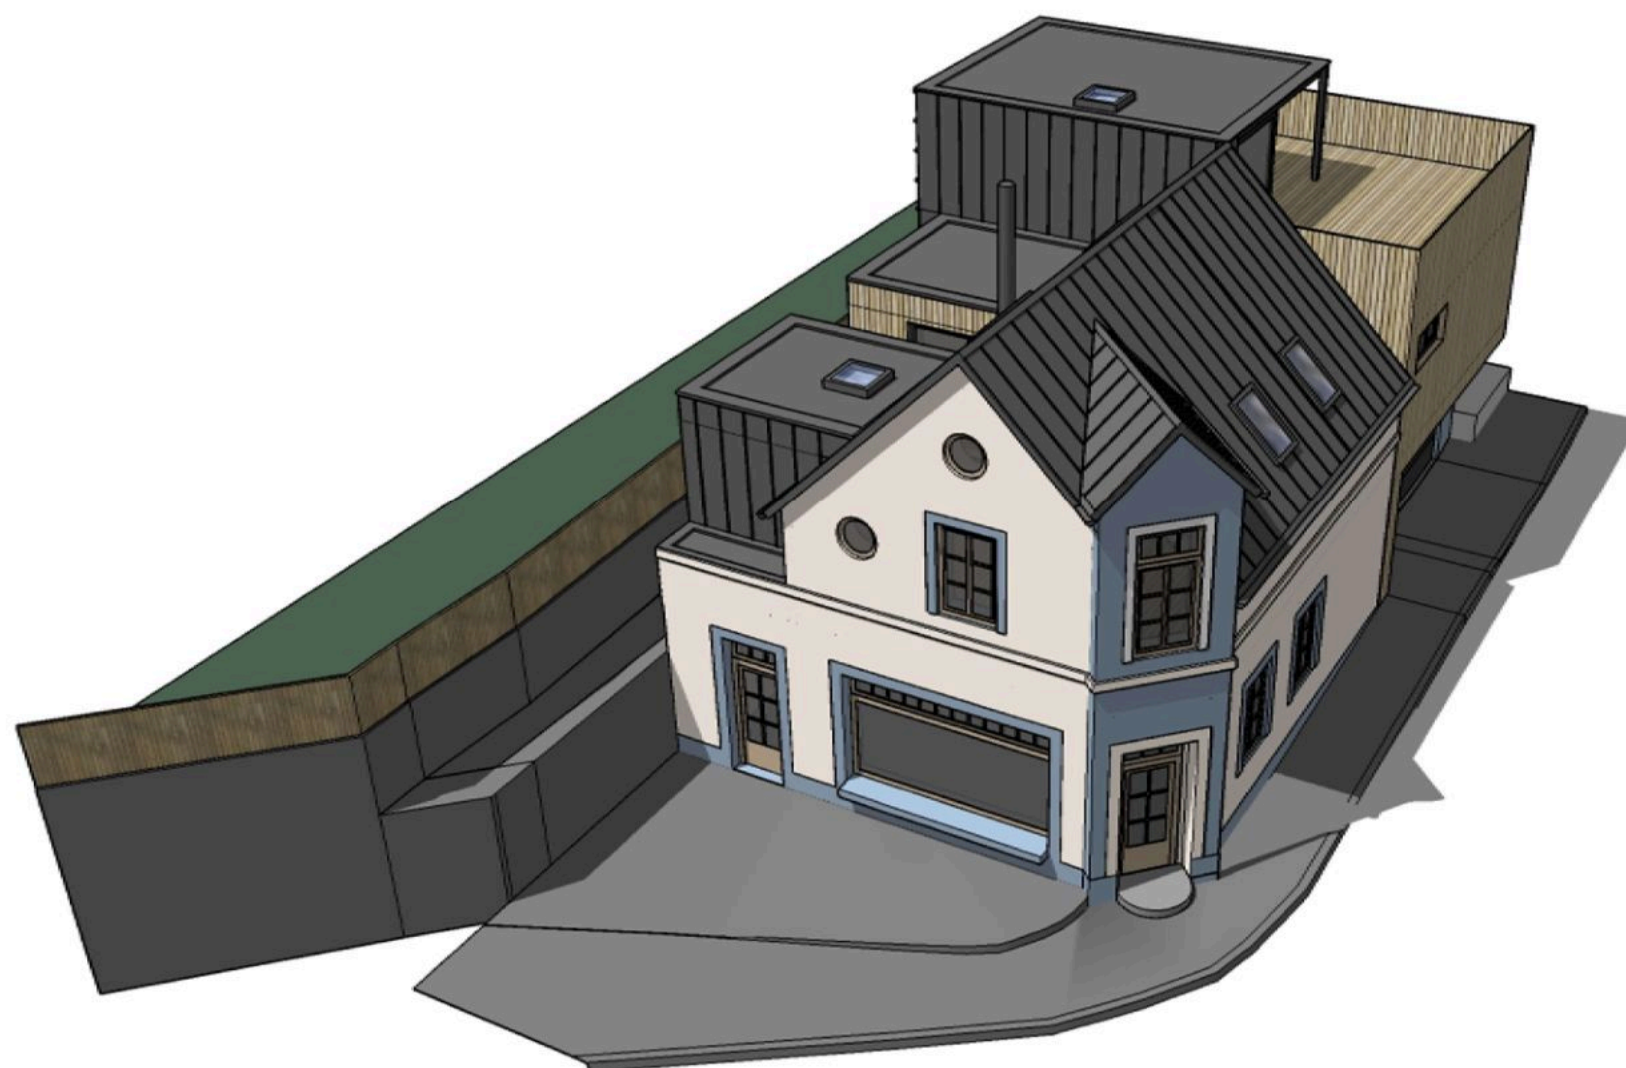

RODINNÝ DŮM S PROVOZOVNOU
VRANOVÉ II 09-2025